


68366551AA

ASF CONTROLLED WHEN RED

ASF Engineering Approved 5/21/24

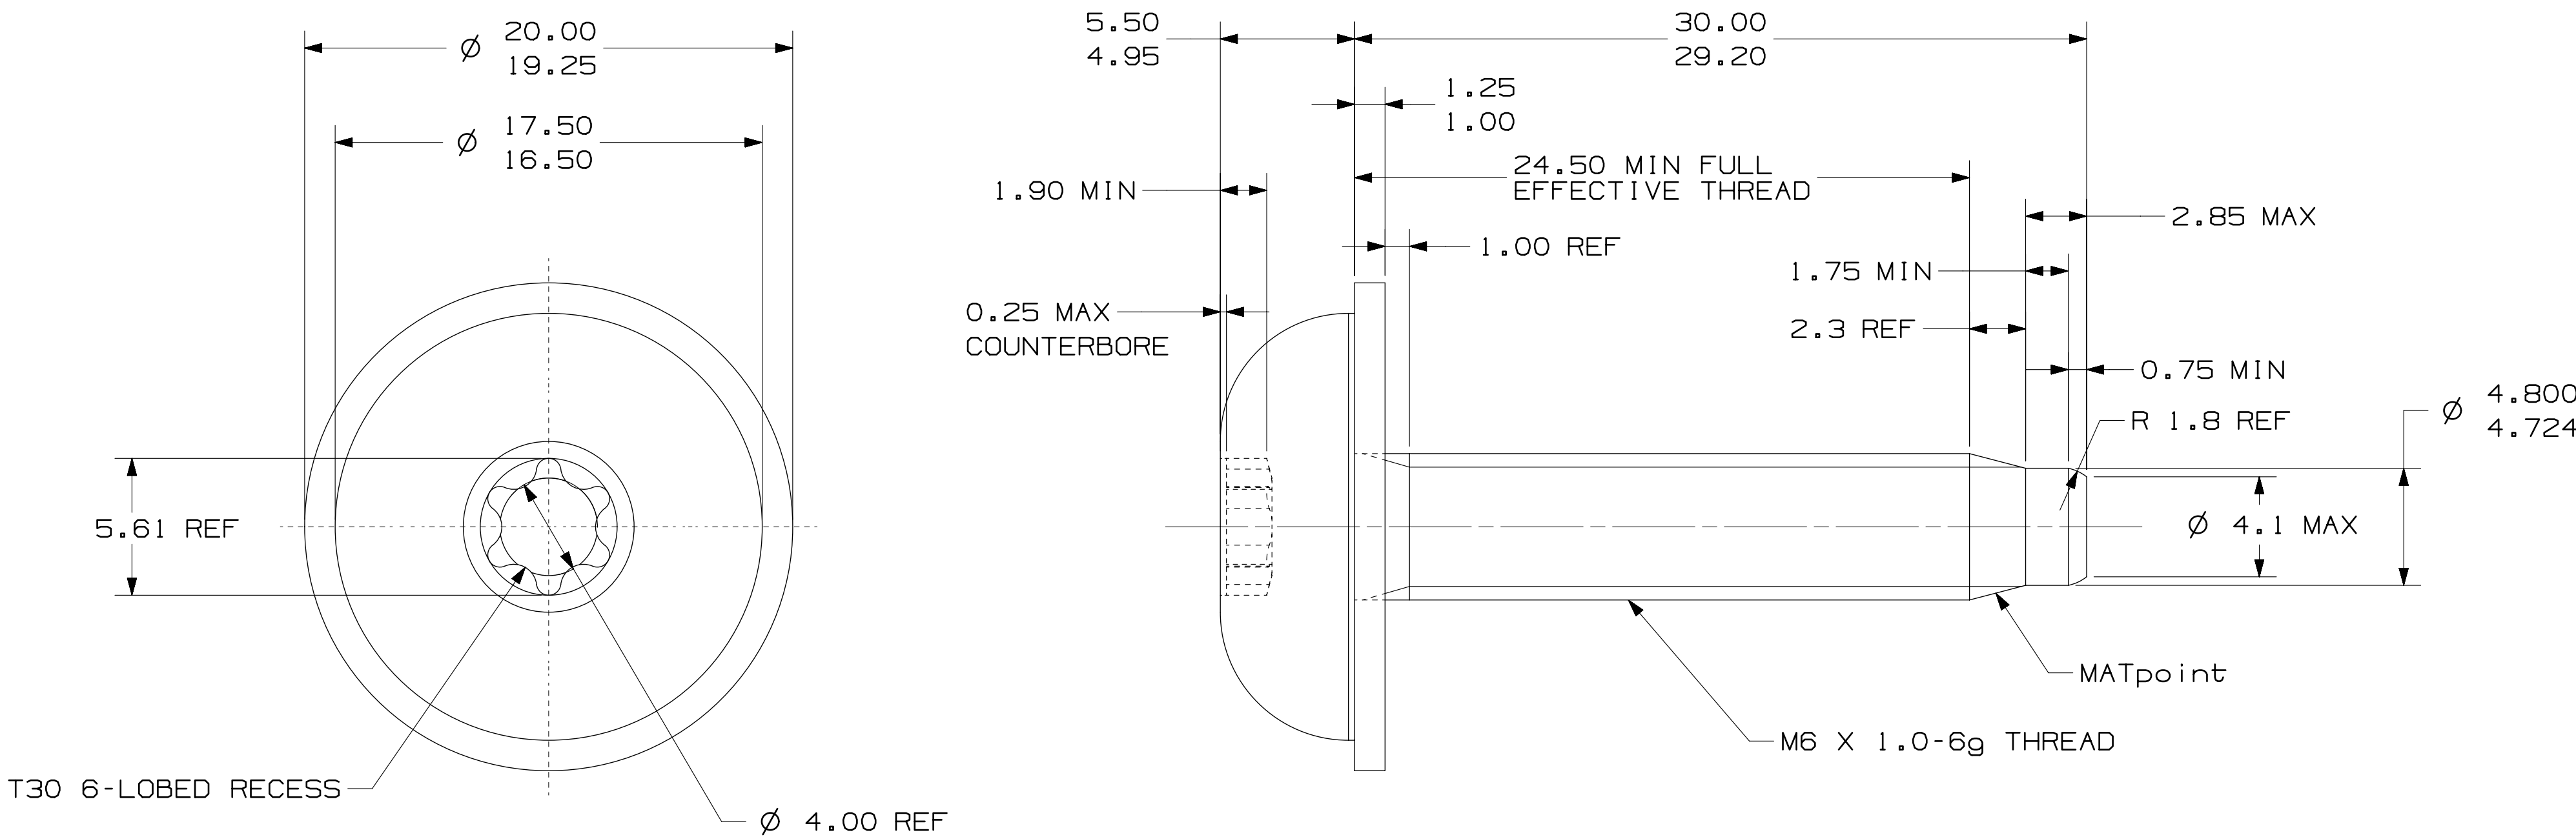

NOTES:

TAMPER RESISTANT FEATURES AND TOOL AT SUPPLIER CHOICE.

PREFERRED TAMPER RESISTANT FEATURES DISPLAYED.

AUTHORITY -		ENGINEERING AMIR KAZEMI		RELEASE DATE	
FCA FIAT CHRYSLER AUTOMOBILES				Identificativo TcAE FA00ADC33607	
				Rev 002	
SEE THE PIP FOR: ENGINEERING STANDARDS REVISION HISTORY COMPLETE MODEL HISTORY		UNLESS OTHERWISE SPECIFIED DIMENSIONS ARE IN: MM		DISEGNO ESEGUITO CON Non sono ammesse variazioni o modifiche manuali	
THIS IS 100% NX GENERATED PART. THE NX MATHEMATICAL DATA IS THE MASTER FOR NON-DIMENSIONED FEATURES.		TOLERANCES: LINEAR: $\pm X . X$ ANGULAR: $\pm X . X^\circ$		Proprieta' FCA ITALY S.p.A. - Senza autorizzazione scritta il presente disegno non potra' essere comunque utilizzato per la costruzione dell'oggetto rappresentato ne' venire comunicato a terzi o riprodotto. Le Societa' proprietarie tutelano i propri diritti o rigione di legge. L'apposizione di qualsiasi marchio appartenente a FCA su prodotti non autorizzati dal titolare, costituisce illecito penale oltreche' civile. All property rights reserved FCA ITALY S.p.A. - This drawing shall not be reproduced, or in any way utilized, for manufacture of the component or unit herein illustrated and must not be released to other parties, without written consent. Any infringement will be legally pursued. Use of any trademark belonging to FCA on products not authorized by the owner is a criminal offense besides civil.	
FOR DIMENSIONAL INFORMATION NOT SHOWN ON THIS DRAWING ANALYZE THE NX MODEL.		REL. FOR PROD. MODELS 2018 VF 001		PCL A	
THIRD ANGLE PROJECTION		DWN JP		SCALE 5:1	
TITLE SC&WA/PAN.HD.FLAT.W ASH.MAT.PT.6-		ALN NUMBER		EBOM PART NUMBER 68366551AA	
ESTIMATED WEIGHT: 0.017 kg					

Massa (Mass)	0.011	Scala (Scale)	3 : 1	Dis. (Drawn)	TOFAS	Cont. (Checked)	YORULMAZ	Marchio (Mark)	NO	Data (Date)	14/02/2017
Cap./N.P. (P.S.)	/	Availo (Confirm)		Vincoli		/	Est./Qual.	/			
TECNOLOGIE				Scat. (Suspended)		/	S.P.	/			
Condiz.				Struttura		E	Foglio (Sheet)	/			
SCREW &WA/PAN.HD.FLAT.WASH.MAT.PT.6-LOBE.REC				Tip (Type)	6363S.01AA.01.S		FCA				
SC&WA/PAN.HD.FLAT.WASH.MAT.PT.6-LOBE.REC				Mat. (File No.)	S26392		A1		EMEA BODY		
C/C	C.F.	CG06		52088199							

06514058AA
ASF CONTROLLED WHEN RED
ASF Engineering Approved 9/1/23

PART INFORMATION PAGE FOR ITEM NUMBER : FC00ACK65887

TITLE BLOCK INFORMATION

Item Number	FC00ACK65887
Item Revision	001
PCL	A
CN	
Item Name	STUD MACHINE THD HEADER PT LOCK PATCH SPECIAL
Item Description	M8X1.25X45.00
Chrysler Part Number	06514058AA
Fiat Codep Number	
Shown-on Part	06514058AA
Status	FA_STEP5,CAD_Released
Owner	LARSEN PAUL (t3300pl)
Engineer	ALL,FASTENERS(T5850XX)
Designer	
Checker	

ENGINEERING STANDARDS APPLIED

Item	Standard No.	Designation	Standard Title
1	PS-4480	(1)	IDENTIFICATION & BAR CODING OF PARTS
2	CS-9800		GENERAL REQUIREMENTS OF MATERIAL STANDARDS AND FCA
3	PF-8500		REQUIREMENTS FOR VERIFICATION, VALIDATION AND CONT
4	PS-9227		CAD/CAM DATA EXCHANGE POLICY
5	CS.00080		FCA CAD STANDARD - GLOBAL REQUIREMENTS
6	CEP-045		MANDATORY AND DISCRETIONARY ENGINEERING STANDARDS
7	CS.00022		GENERAL REQUIREMENTS FOR RELEASED DRAWINGS
8	CS-11000	(1)	TRADEMARK IDENTIFICATION ON PARTS - 01446_22_00053
9	CS-9003		SUPPLIER REQUIREMENTS FOR VEHICLE AND SERVICE PART
10	PS-10052		INFORMATION SECURITY
11	MS.50077<S>	8.8	EXTERNALLY THREADED FASTENERS FOR NORMAL USE (HARM
12	PS.50031	c8 plain	ZINC NICKEL ALLOY ELECTRODEPOSITED COATINGS
13	01307		STEEL BOLTS AND NUTS - Representation, designation
14	PF.90348<S>		INSPECTION OF THREADED FASTENERS FOR NORMAL USE AN
15	PS-7099		GENERAL SPECIFICATIONS - FASTENERS AND FITTINGS

SPECIAL CHARACTERISTICS BLOCK

APPEARANCE	N	DIAMONDS	N
EMISSIONS	N	HOMOLOGATION	N
SAFETY	N	TRACEABILITY	N
OTUP	N		

GENERAL ENGINEERING NOTES (OPTIONAL)

INITIAL RELEASE

PART CHANGE BLOCK

CN	PCL	Originator	CN Decision Date	TC Rev	TC Official Release Date	CN Description	Comments
	A			001	2023-04-19		